

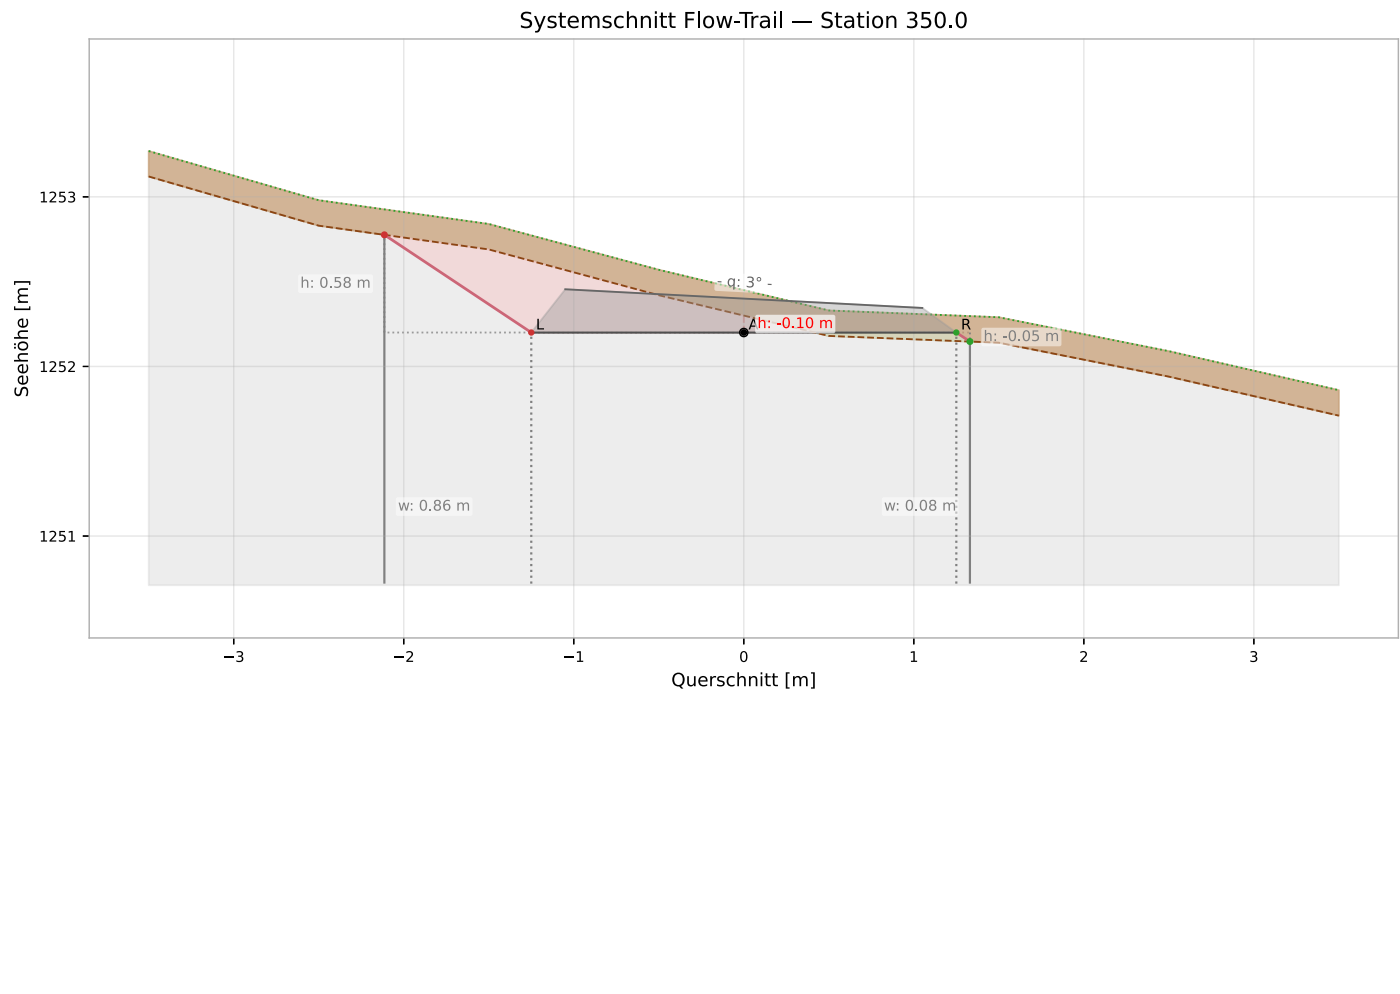
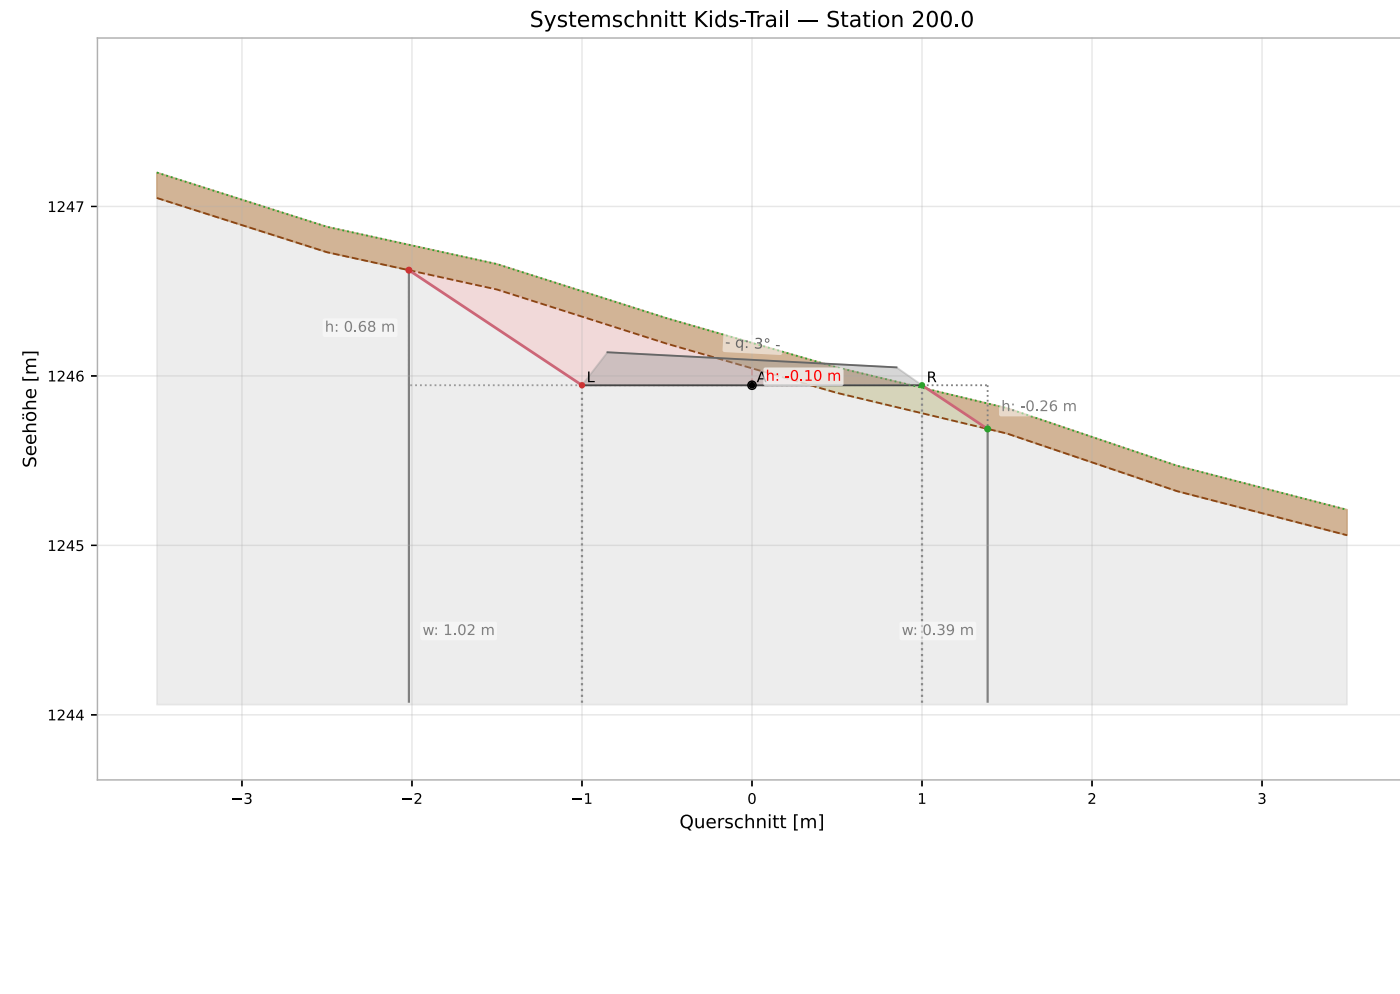
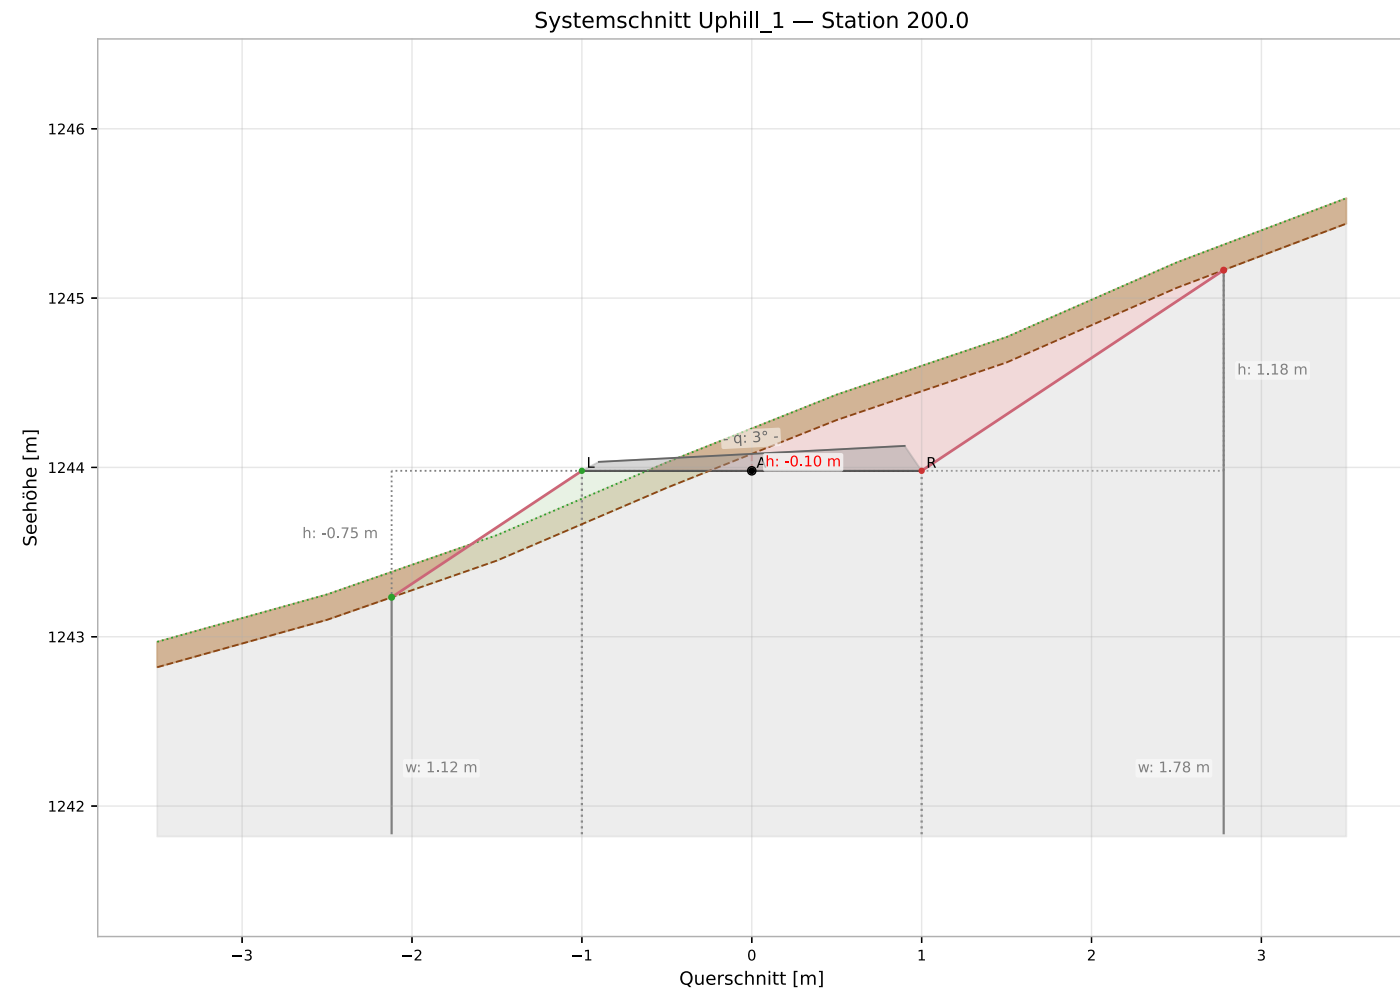
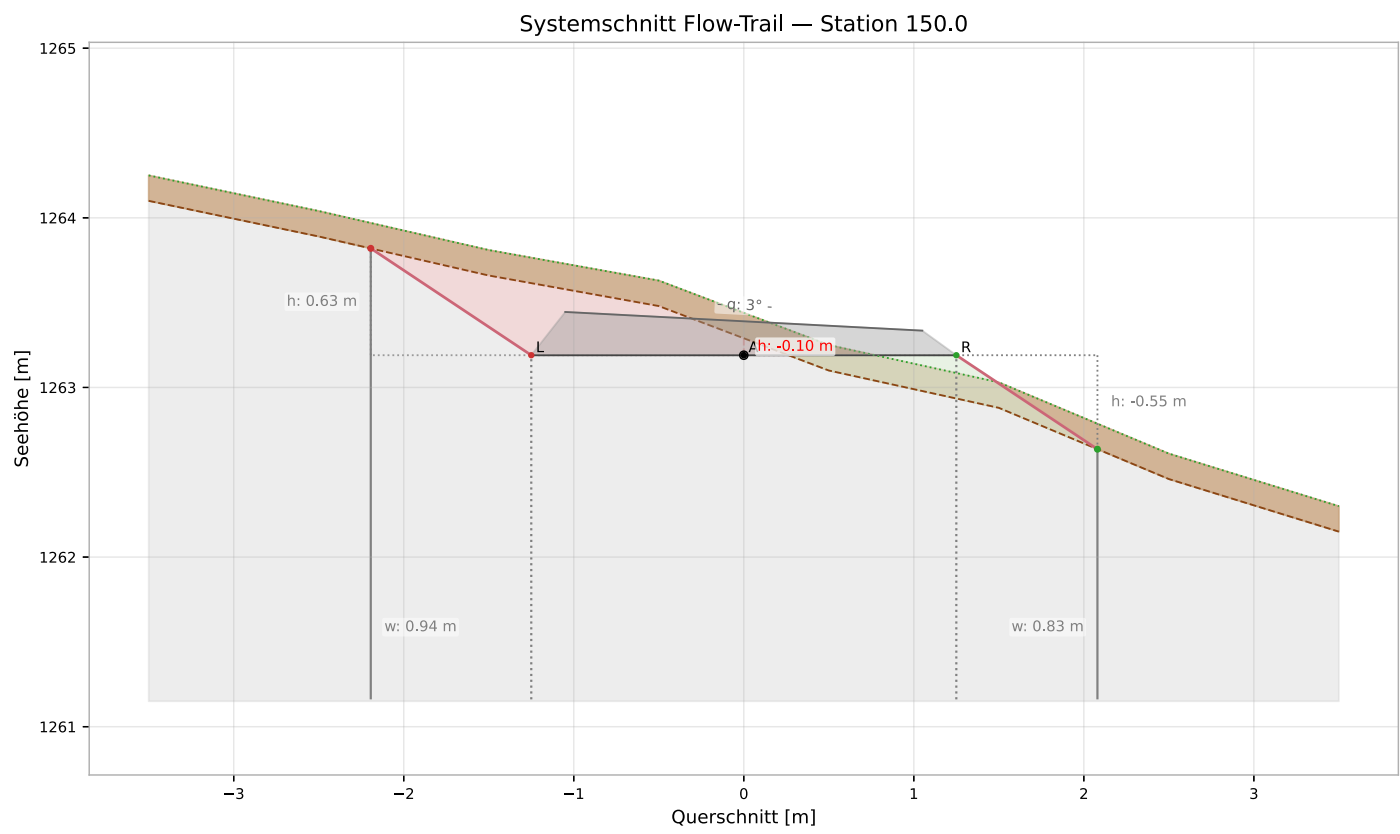


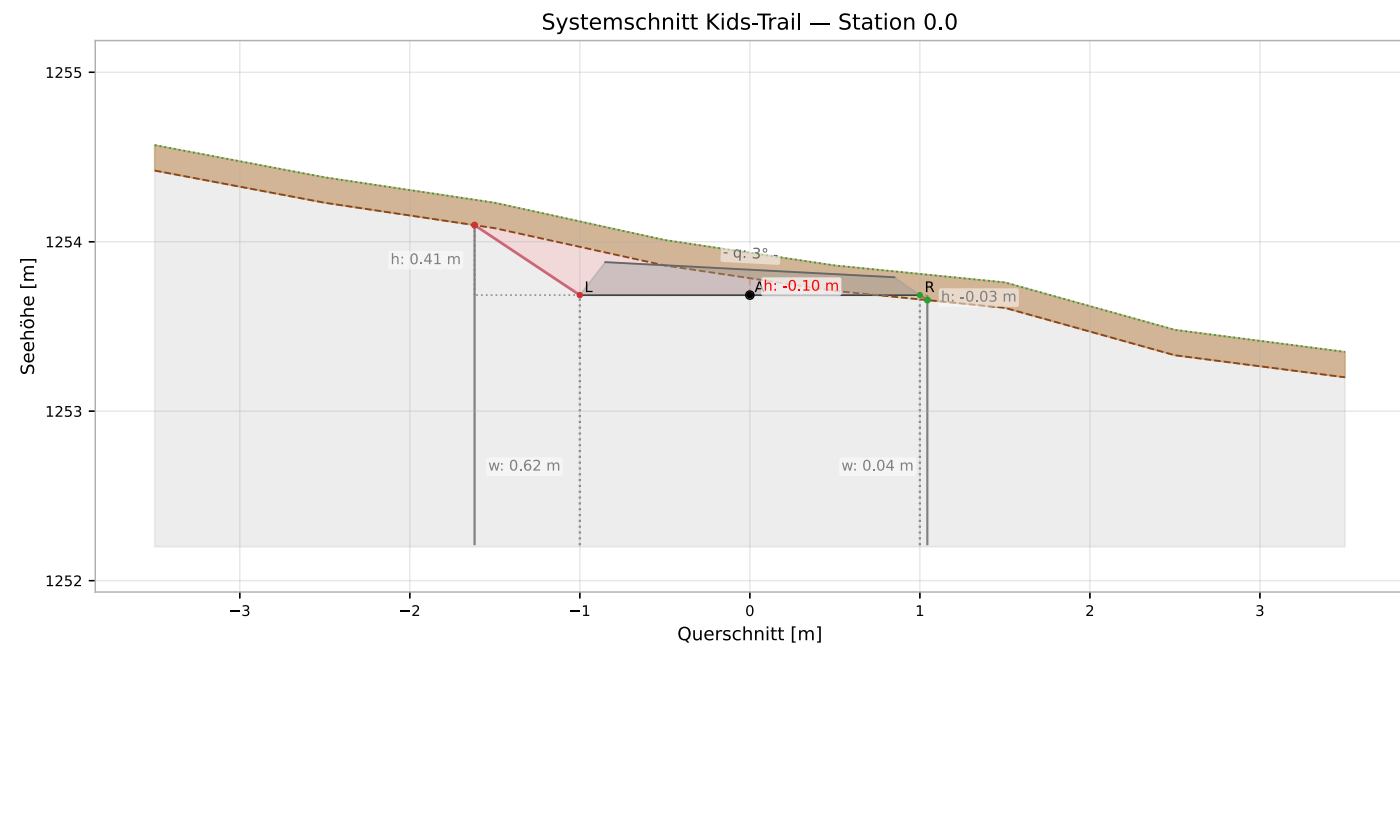

Systemechnitte
(Auswahl, Planum = Fahrbahnbreite + 0,5 m)

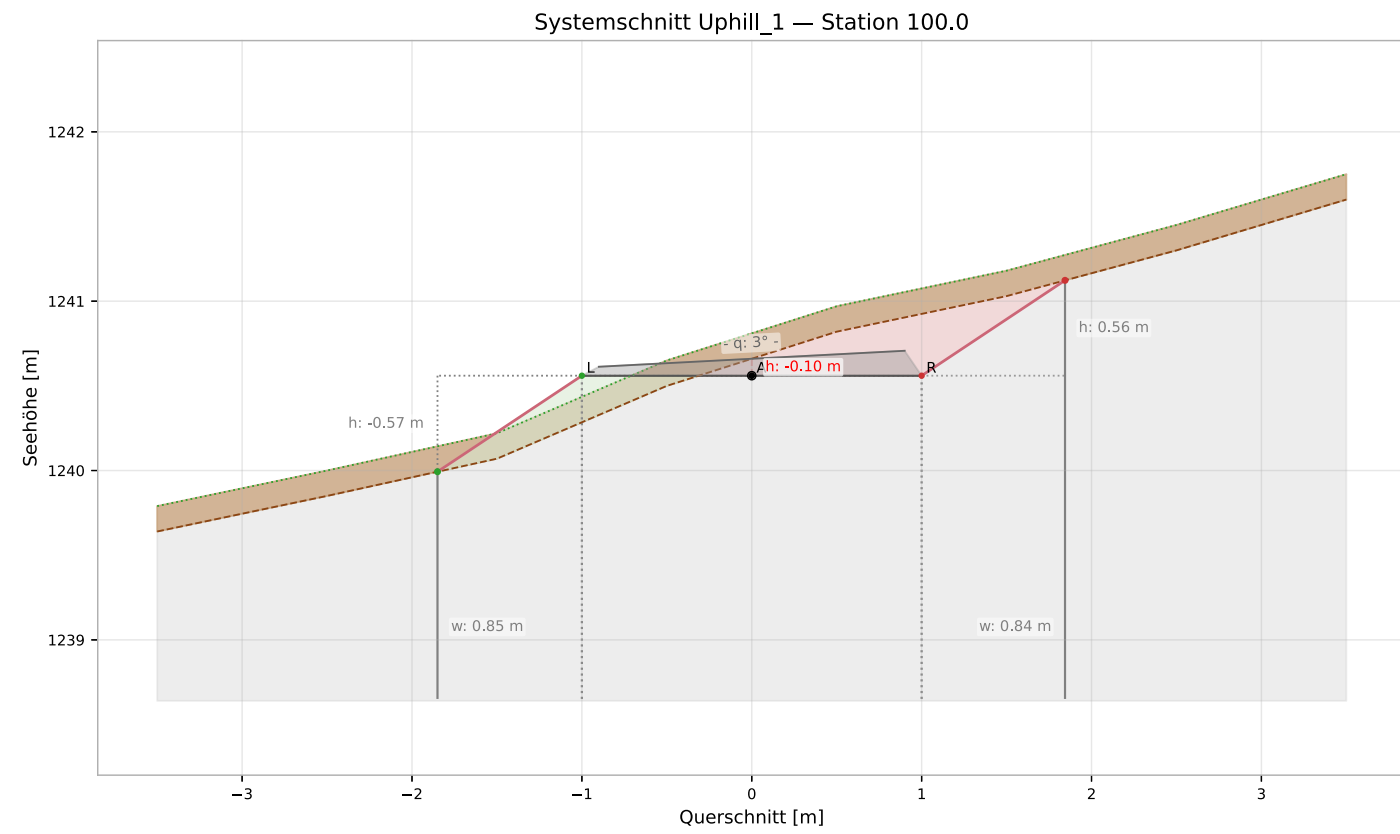

Technische Daten Trails

Name	Klasse	Breite [m]	Länge [m]	Längsgefälle [%]	Deckschicht [m]
Flow-Trail	leicht	2	616	-4,5	0,2
Kids-Trail	leicht	1,5	371	-3,7	0,15
Uphill 1	leicht	1,5	463	3	0,1
Uphill 2	leicht	1,5	306	6,1	0,1