


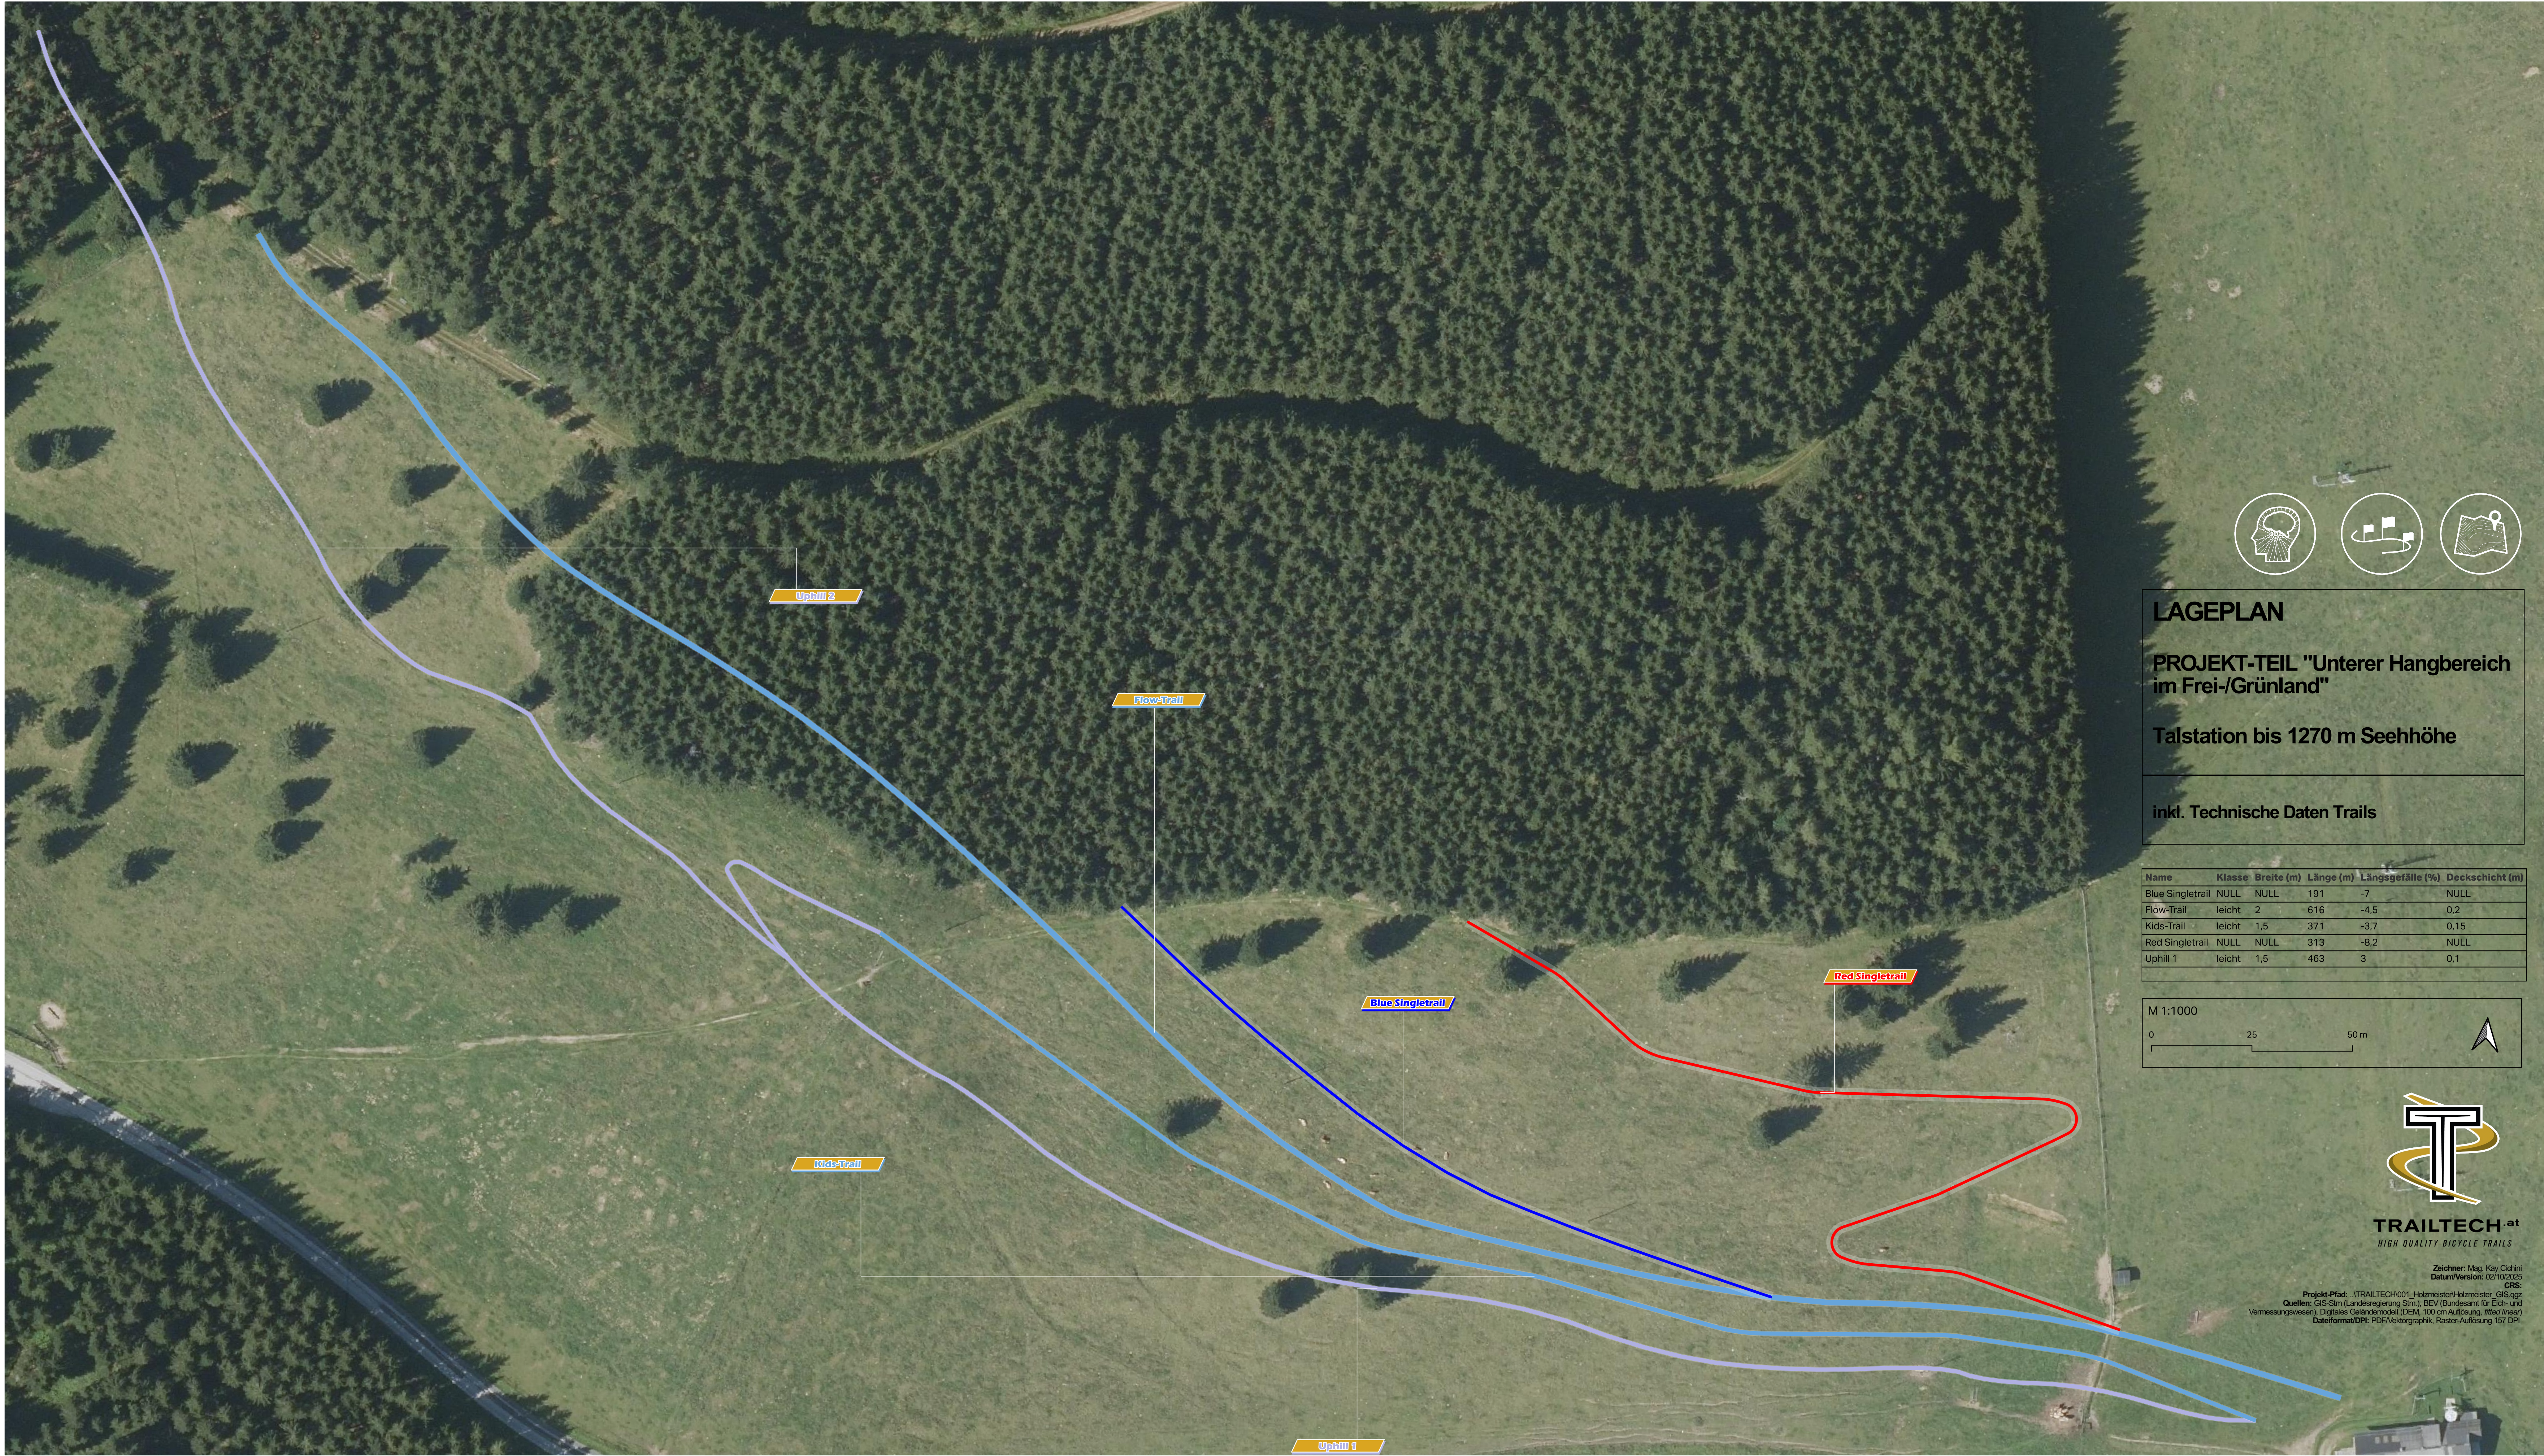


LAGEPLAN

PROJEKT-TEIL "Unterer Hangbereich im Frei-/Grünland"

Talstation bis 1270 m Seeshöhe

inkl. Technische Daten Trails

Name	Klasse	Breite (m)	Länge (m)	Längsgefälle (%)	Deckschicht (m)
Blue Singletrail	NULL	NULL	191	-7	NULL
Flow-Trail	leicht	2	616	-4,5	0,2
Kids-Trail	leicht	1,5	371	-3,7	0,15
Red Singletrail	NULL	NULL	313	-8,2	NULL
Uphill 1	leicht	1,5	463	3	0,1

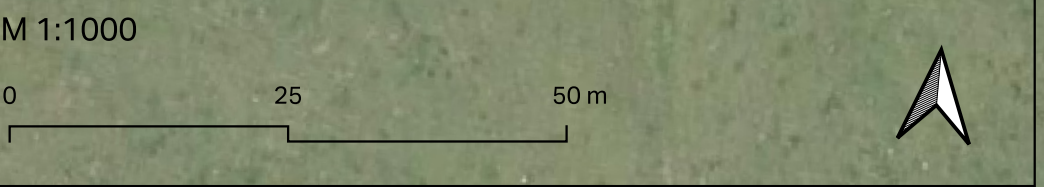

TRAILTECH.at
HIGH QUALITY BICYCLE TRAILS

Zeichner: Mag. Kay Ochini
Datum/Version: 02/10/2025
GRS
Projekt-Plat: .\TRAILTECH\001_Holzmeister\Holzmeister_GIS.qgz
Quellen: GIS-Stm (Landesregierung Stm.), BEV (Bundesamt für Eich- und Vermessungswesen), Digitales Geländemodell (DGM, 100 cm Auflösung, lited/linear)
Dateiformat/DPI: PDF/Vektorgrafik, Raster-Auflösung 157 DPI